
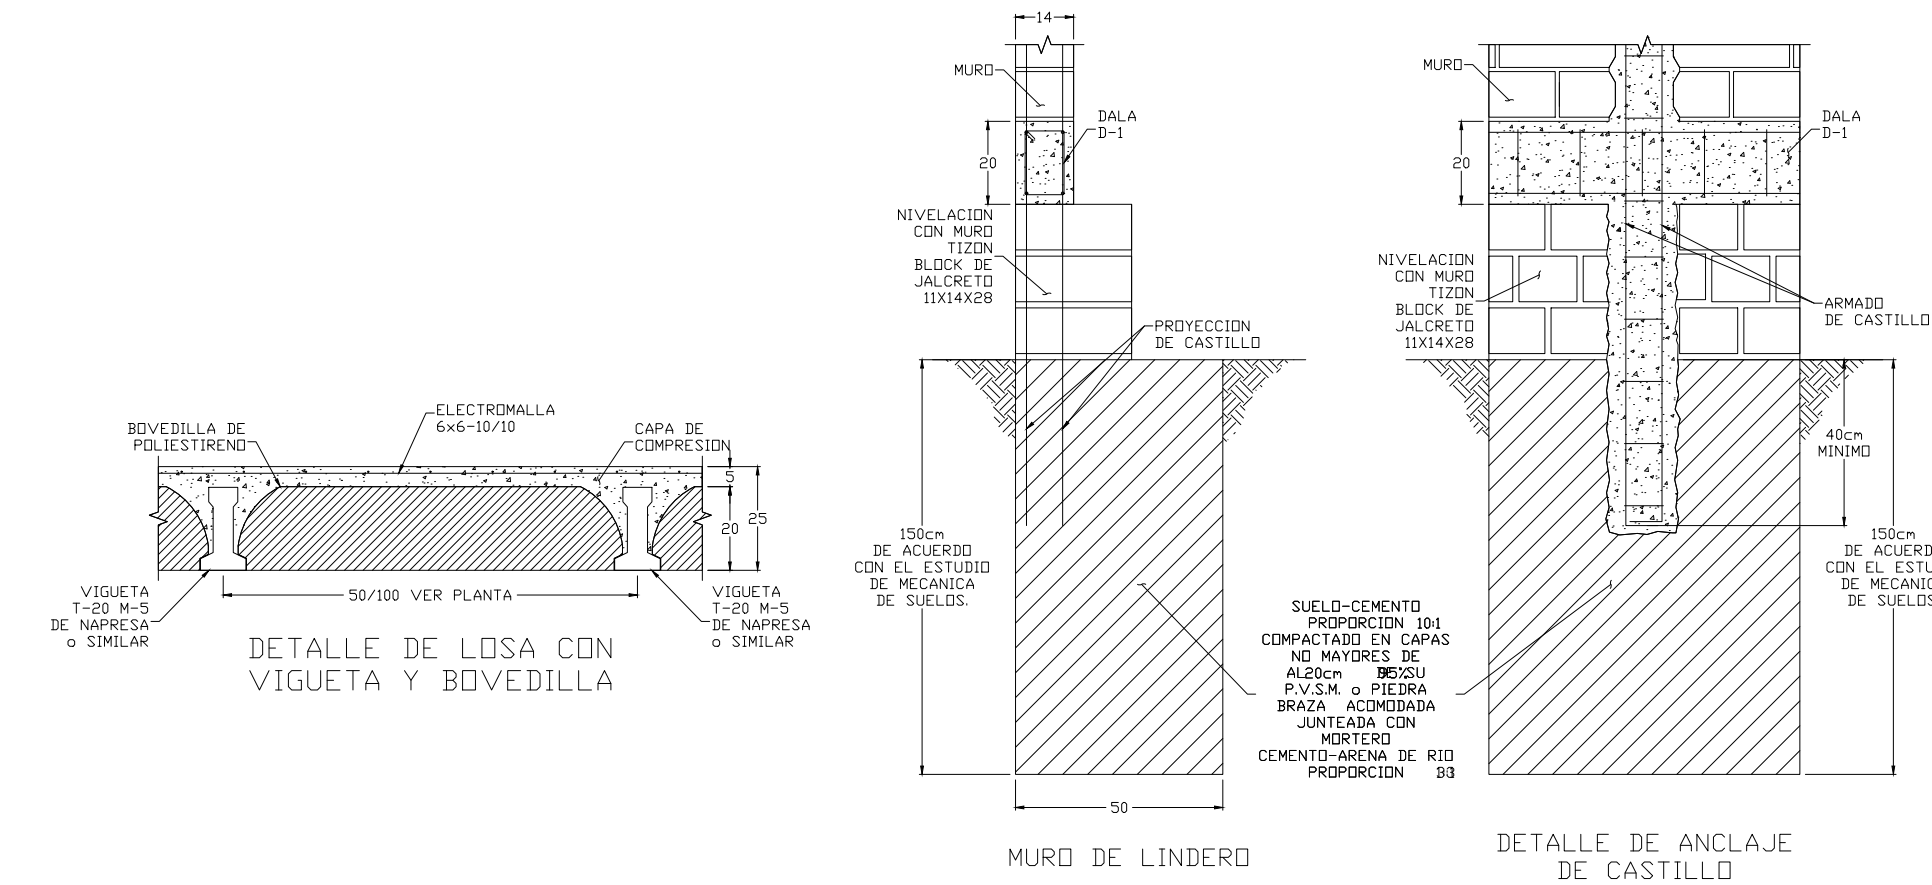
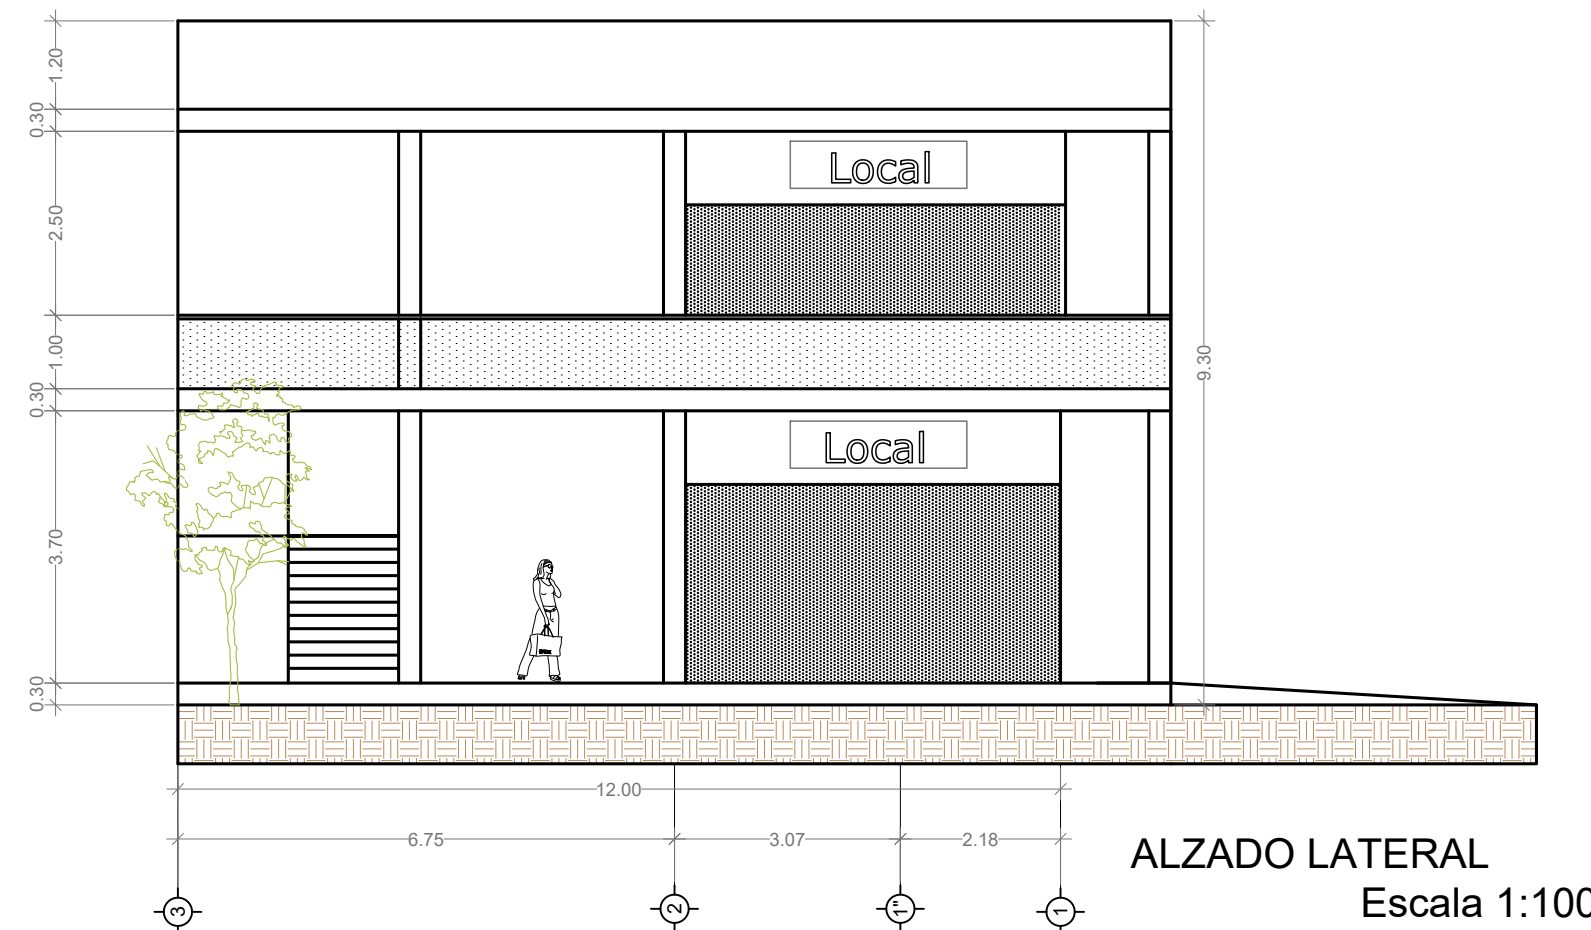
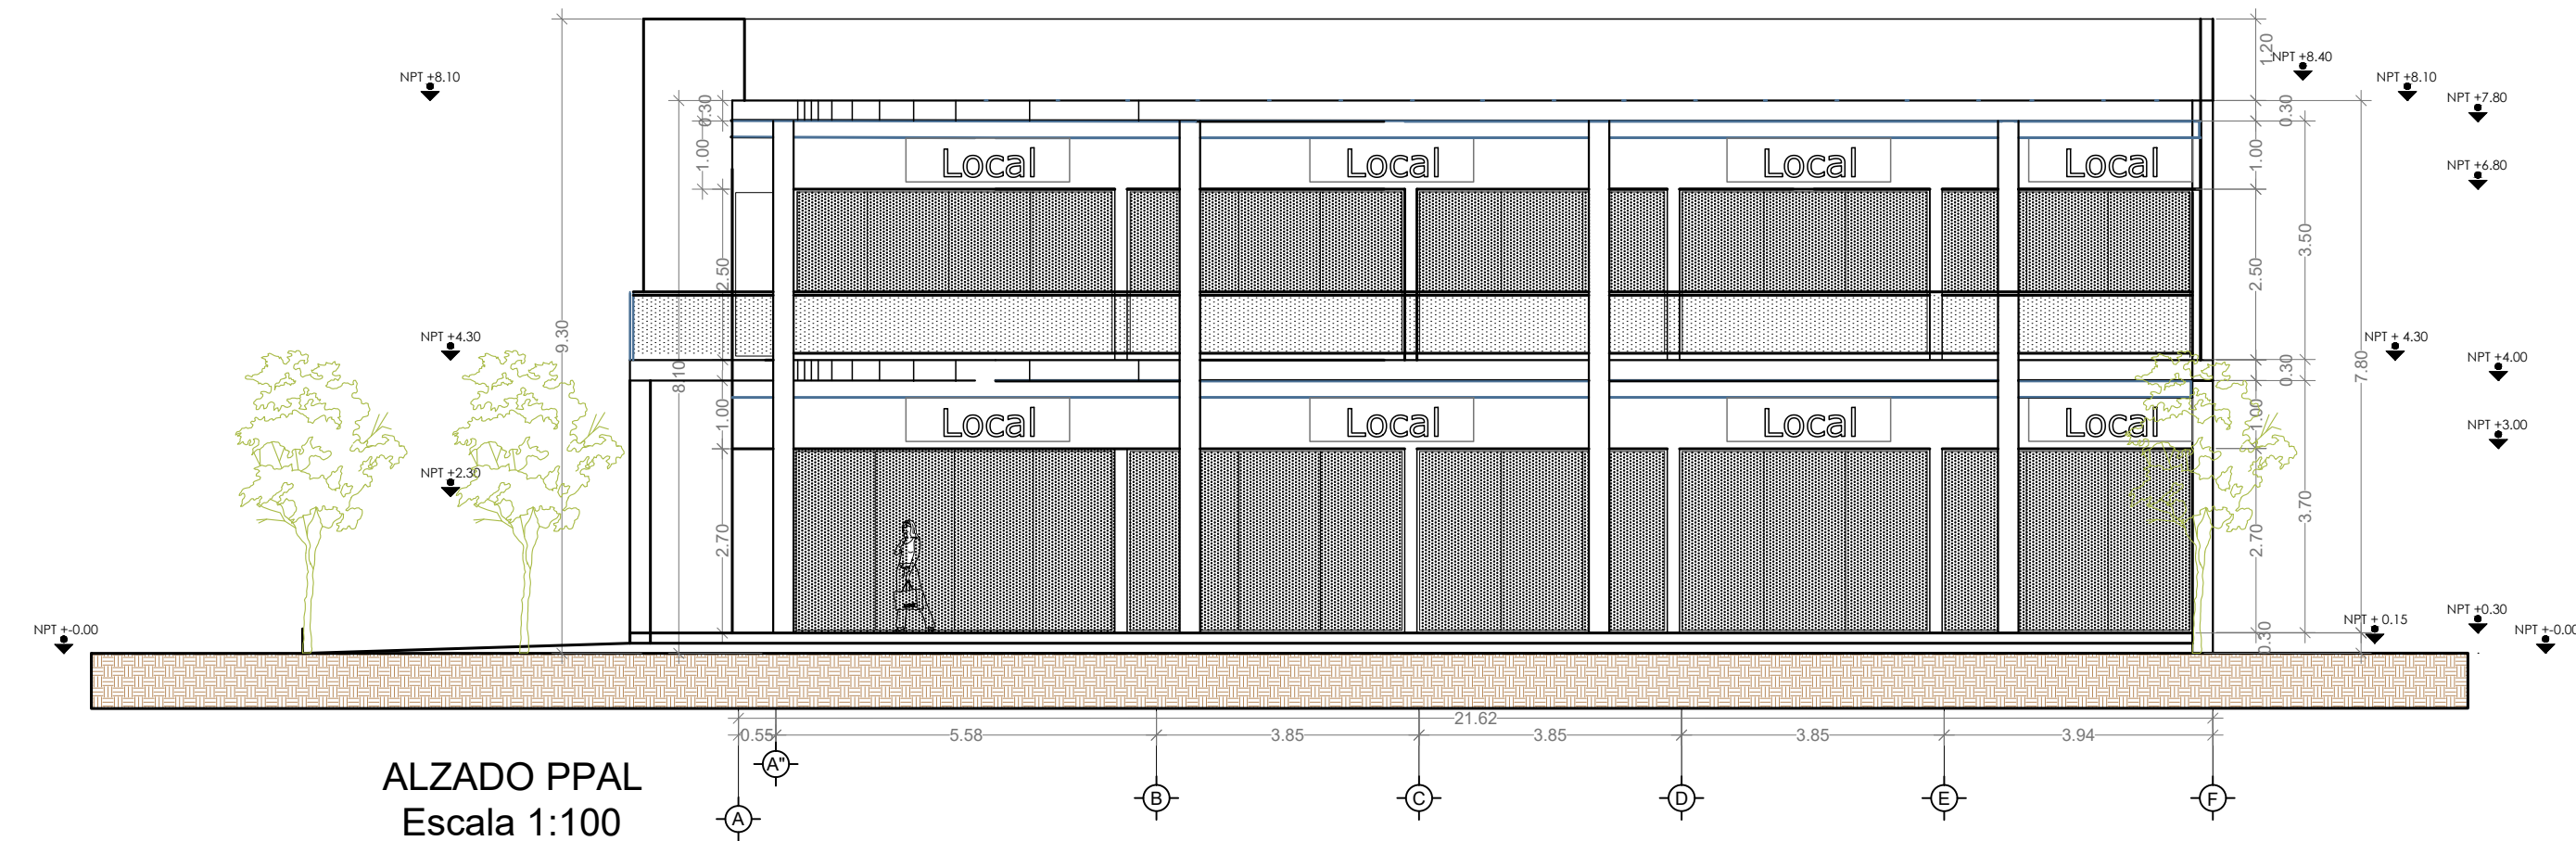
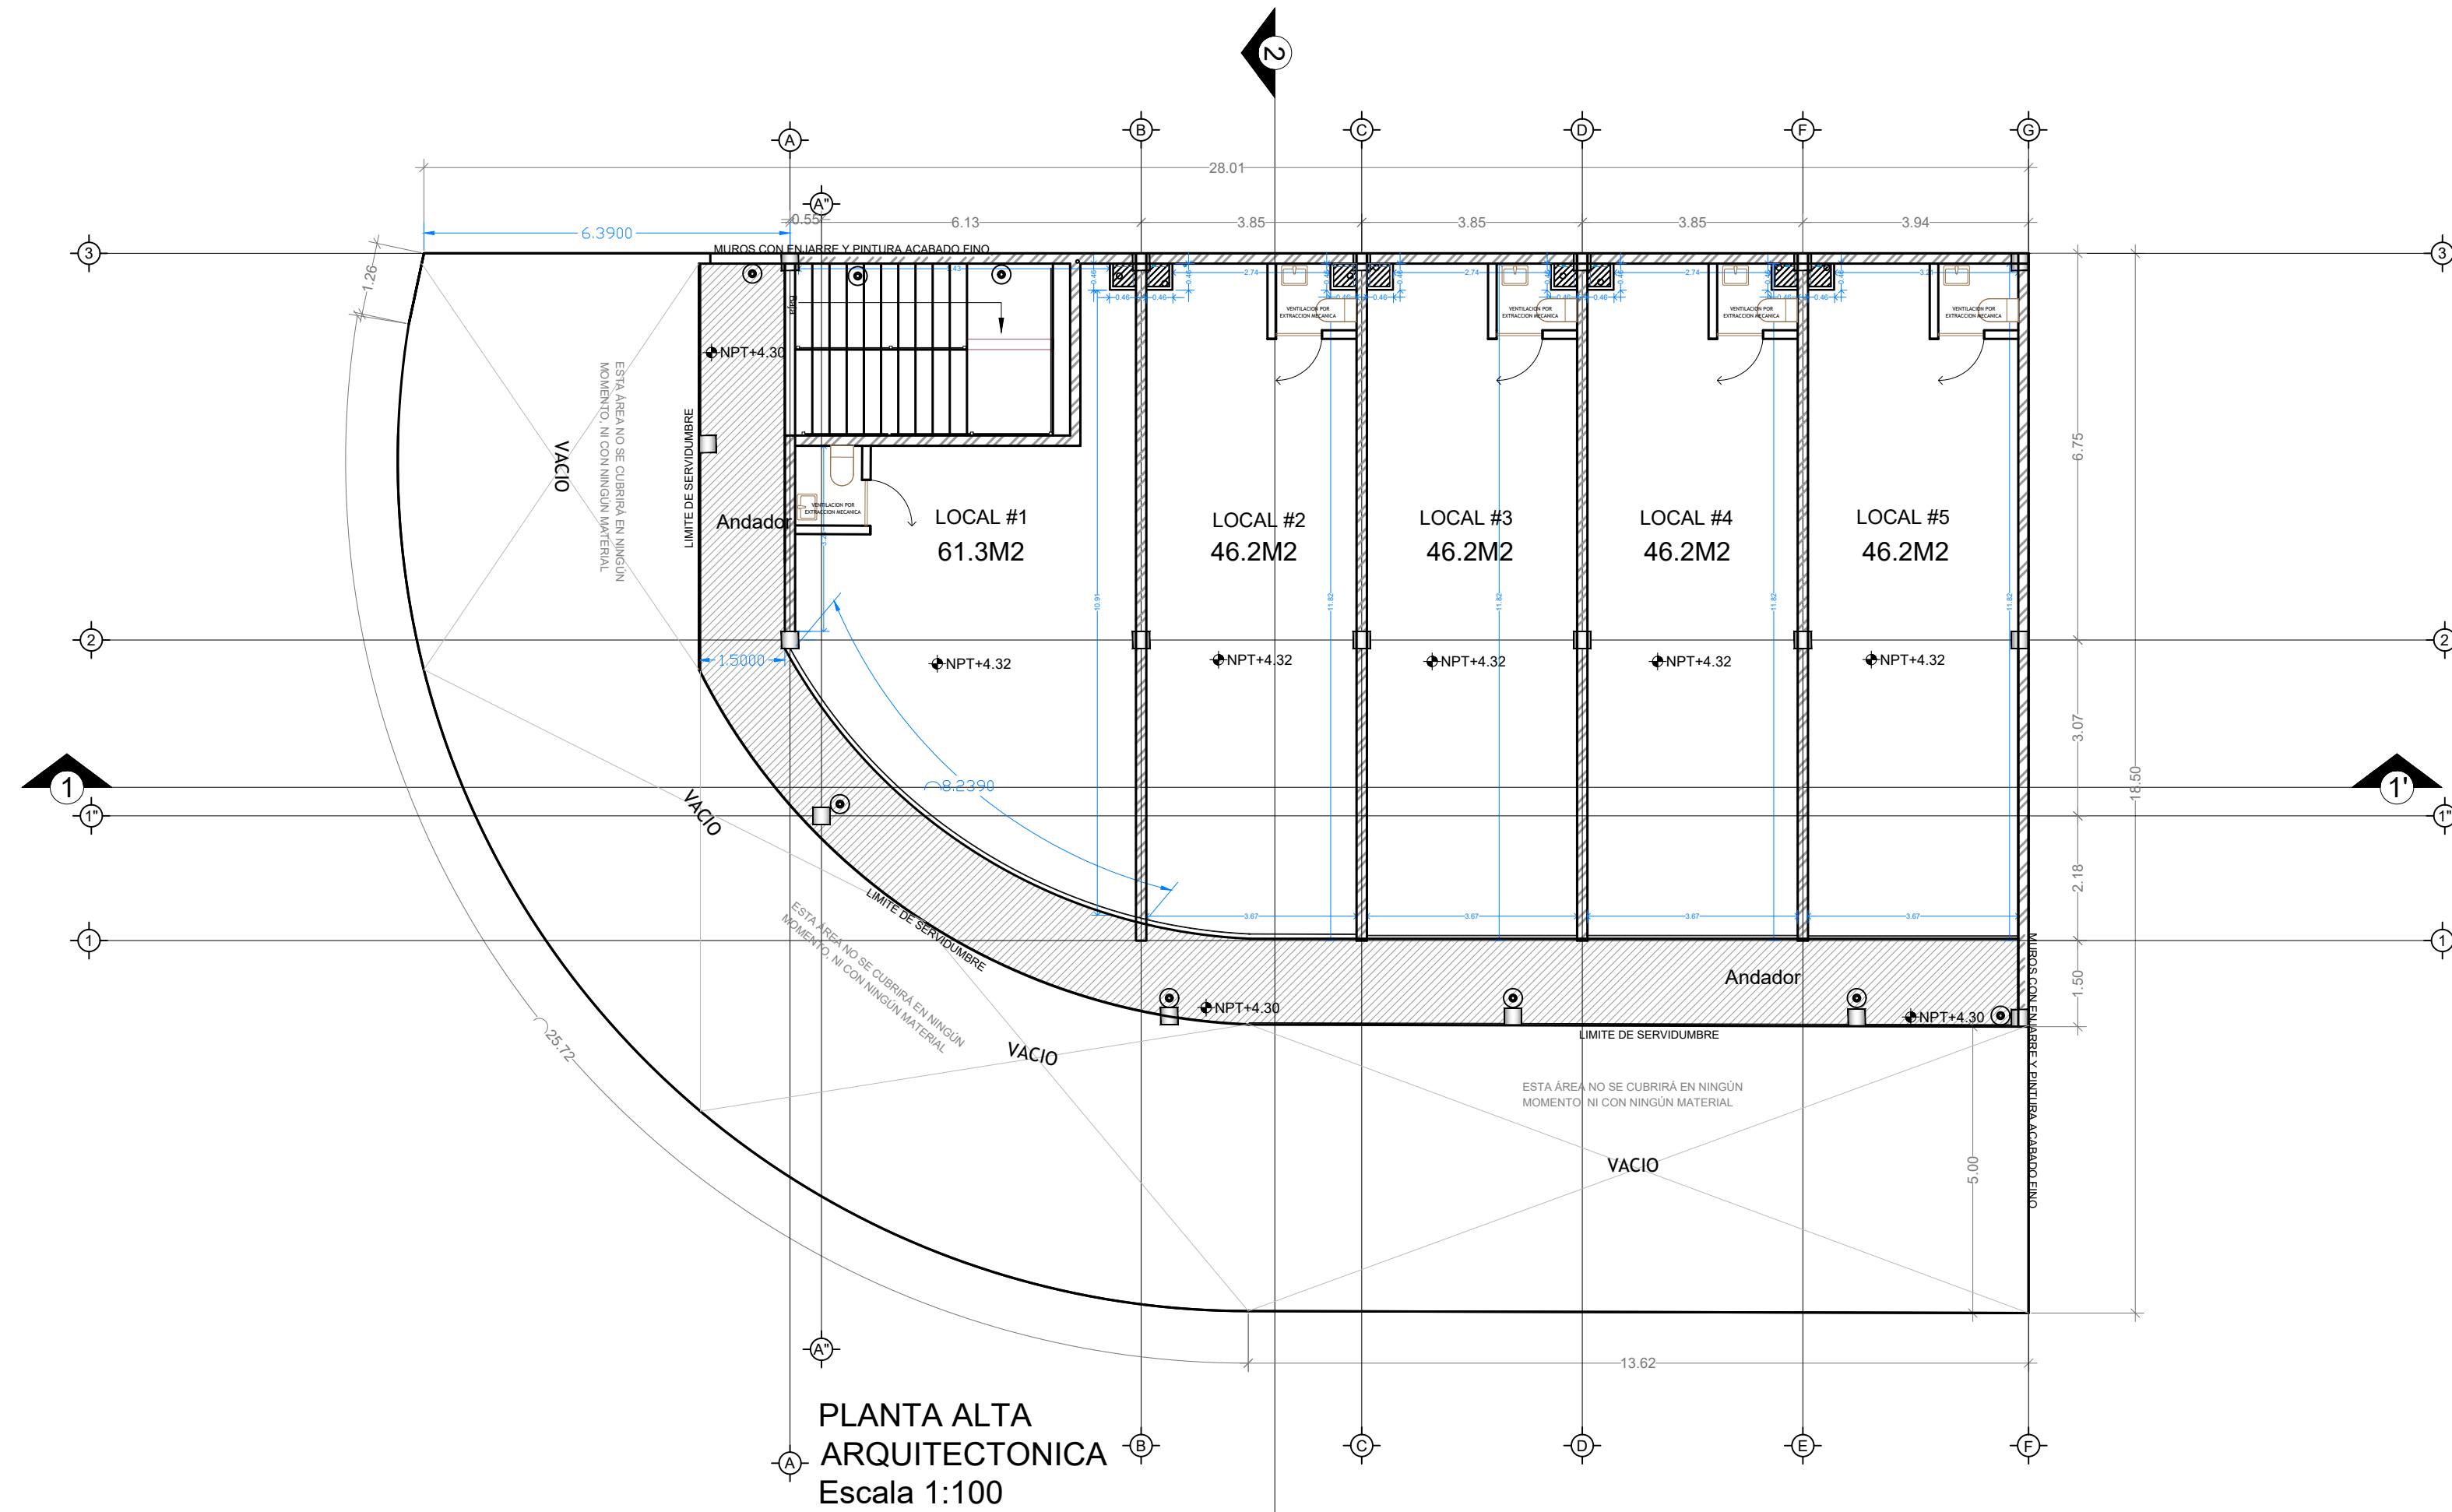


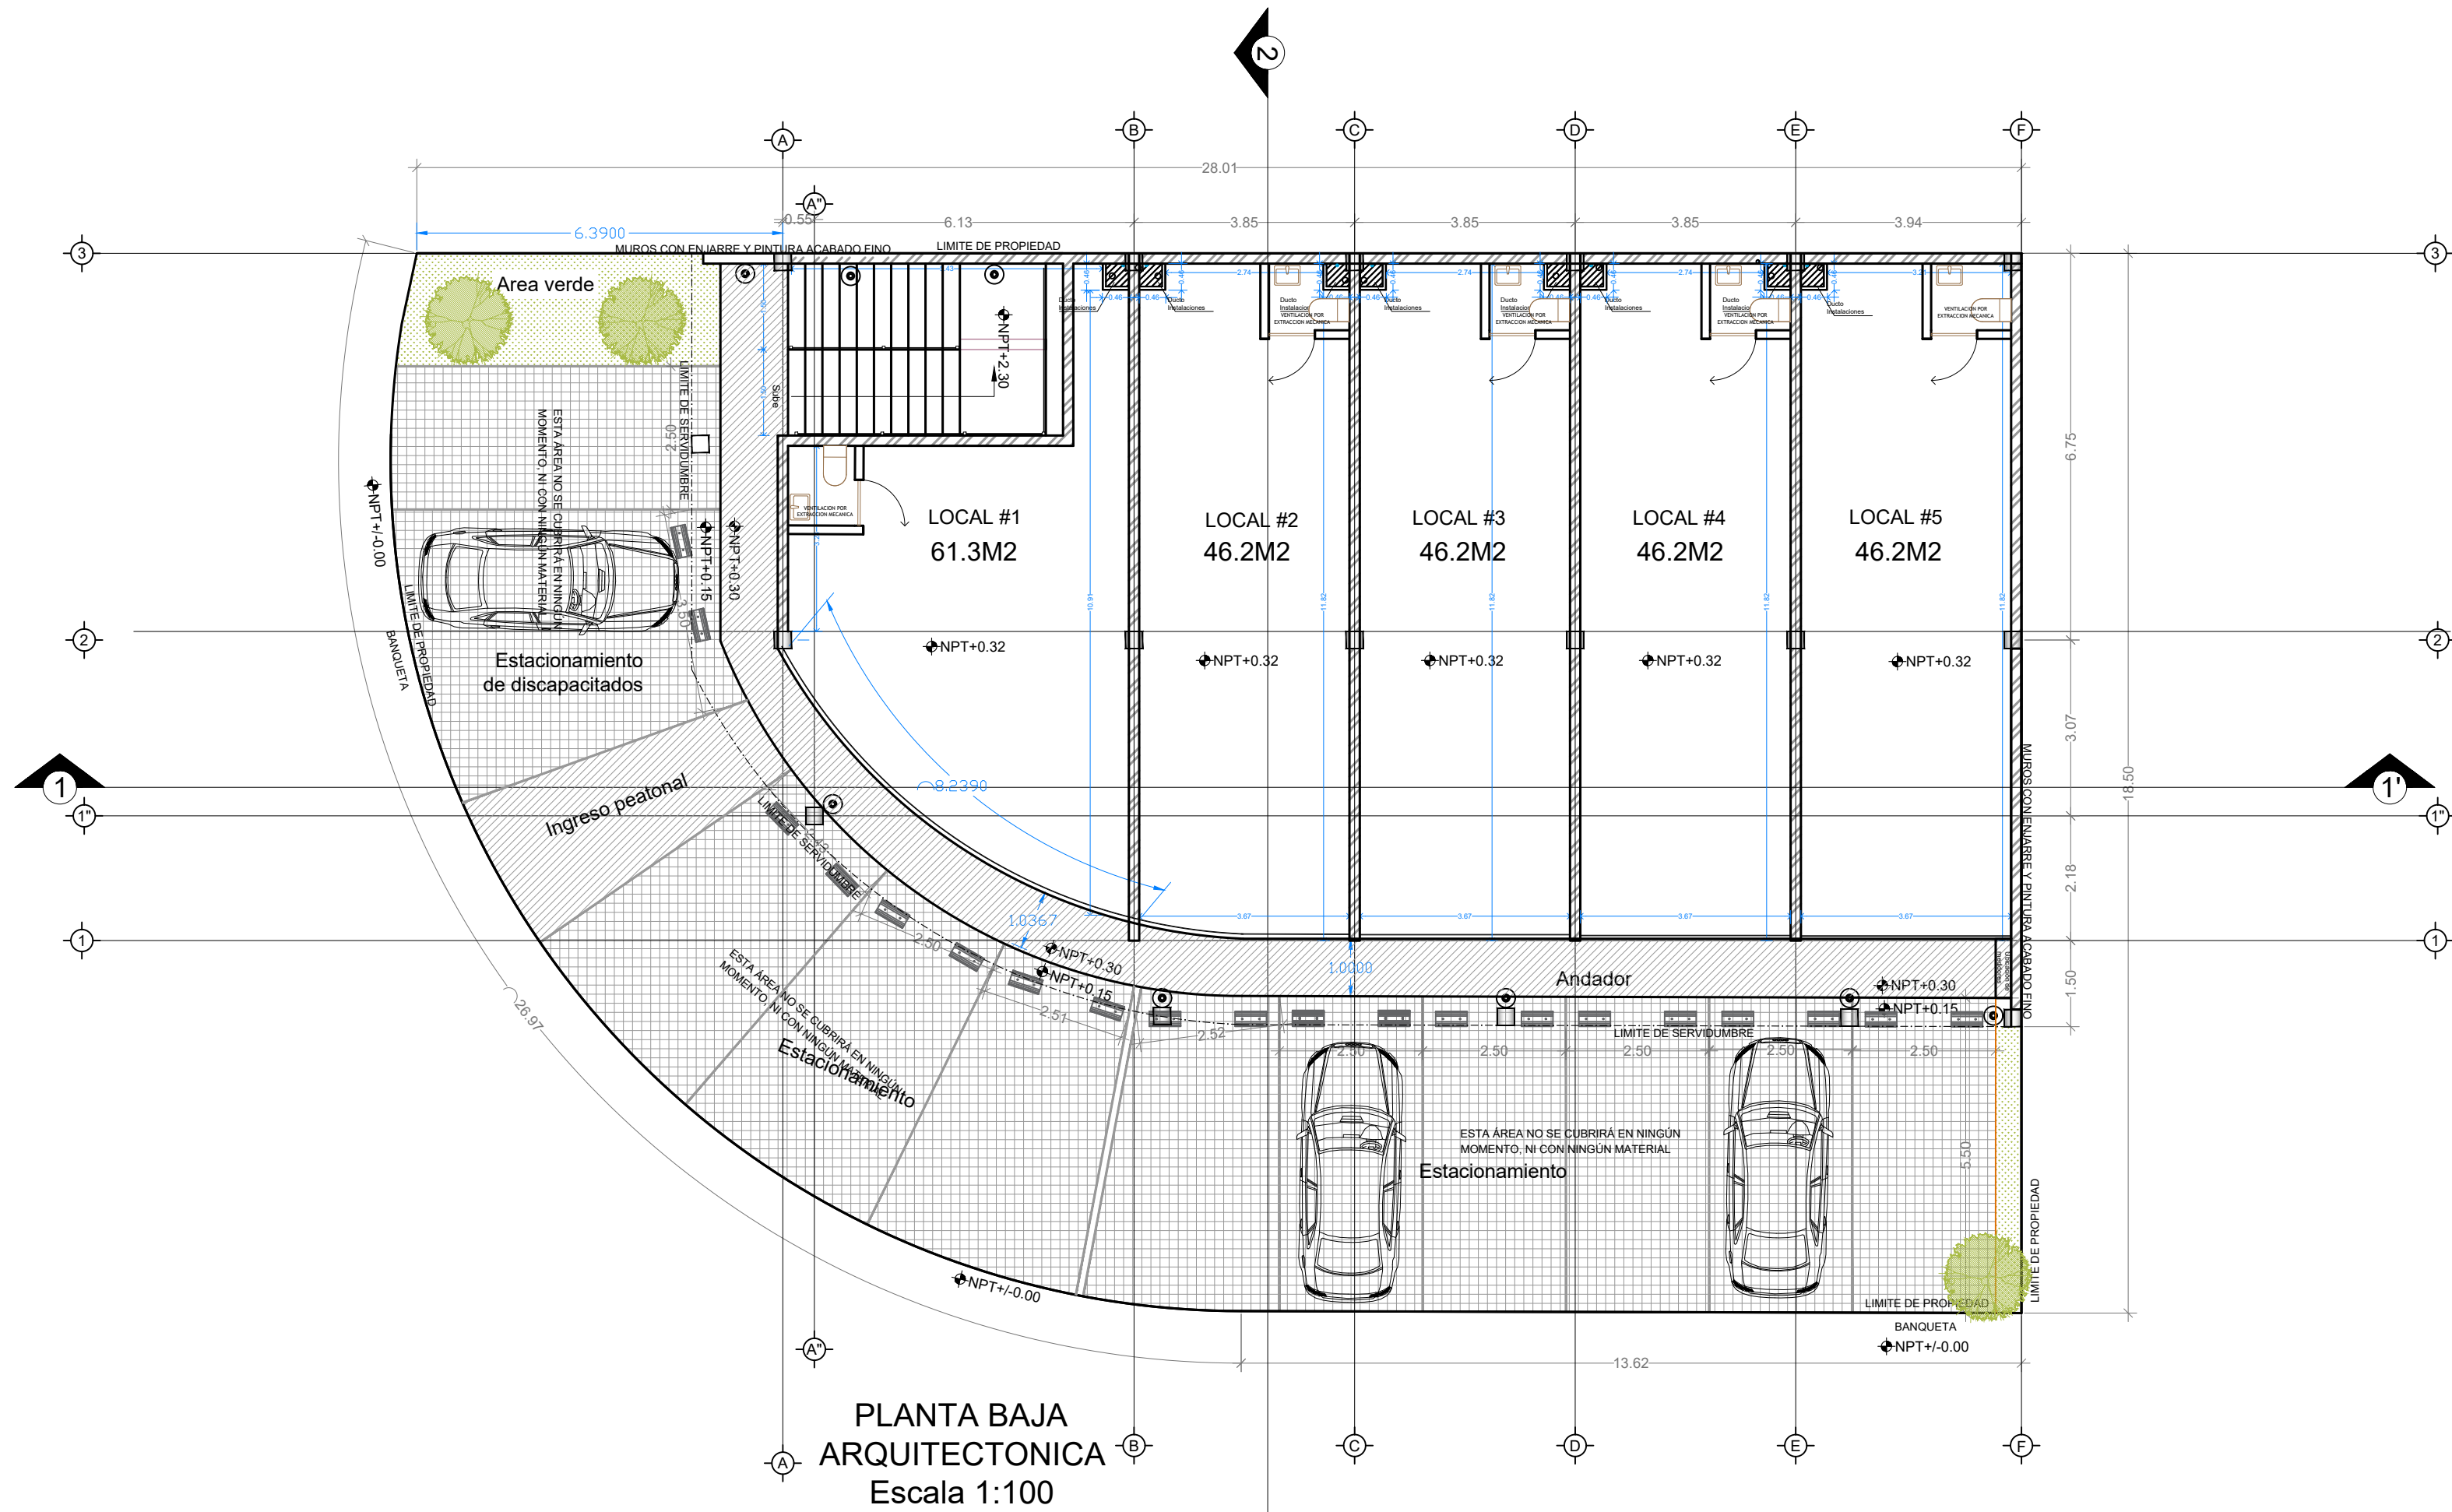

N° Único

N° de control

Dirección del Área de Licencias y Permisos de Construcción

Jefatura de Licencias de Construcción

PLANO DE PERMISOS

Descripción Proyecto

Coefficiente ocupación de suelo (COS) 0.80

Incremento COS

Coefficiente utilización de suelo (CUS) 1.60

Incremento CUS

Cajones de estacionamiento 12

Tipo de obra Comercial

Uso de la obra

Superficie terreno 478.229 M2

Superf. Construcción actual (total)

Superf. Construcción actual (pb)

Superf. Construcción actual (pa)

Superf. Construcción propuesta (pa) 272.82 M2

Superf. Construcción propuesta (pa) 288.51 M2

Superf. Construcción propuesta (2n)

Nota: Añadir desglose por nivel en caso de contar con más

Plan Parcial Desarrollo Urbano

N° de expediente

COS

ICOS

CUS

ICUS

Cajones estacionamiento 10

Cuadro de cargas

Cargas vivas: 200 kg/cm2

Cargas muertas: 380 kg/cm2

Cargas Azotea: 100 kg/cm2

Cargas Total: 425 kg/cm2

Capacidad de carga del terreno: 15.11 Ton./m2

NORTE

Ubicación

478.229M2

SIMBOLOGIA

BAIANTE DE AGUAS NEGRAS

BAIANTE DE AGUAS PLUVIALES

COLADERA DE AGUAS PLUVIALES

TUBERIA P.V.C. CODO

TUBERIA P.V.C. COUPE

TUBERIA P.V.C. TEE

TUBERIA P.V.C. AGUAS PLUVIALES

TUBERIA P.V.C. AGUAS SERVIDAS

REGISTRO

POZO DE ABSORCIÓN

Espacio para sello

Para ser llenado por la dependencia

PROYECTO ARQUITECTONICO

REVISÓ EL PROYECTO

FECHA

Firma

Firma

Director del Área de Licencias y Permisos de Construcción

Jefatura de Licencias de construcción

Licencia de Construcción

Tipo de obra: Locales comerciales

Ubicación: LOTE COMERCIAL 05 (CINCO), MANZANA 03 (TRES), FRACCIONAMIENTO "ALVA" CALLE PASEO DE LA ALBORADA ESQUINA PASEO DEL ALVA

Propietario: RADRO DESARROLLOS INMOBILIARIOS

Representante legal: FRANCISCO OCHOA MADRICAL

Firma:

Director Responsable de Obra o Proyecto

Nombre:

Registro:

Escala: 1:100

Firma:

Nombre archivo: PLAZA "ALVA"

Lámina 1/2